Roof plan — proposed

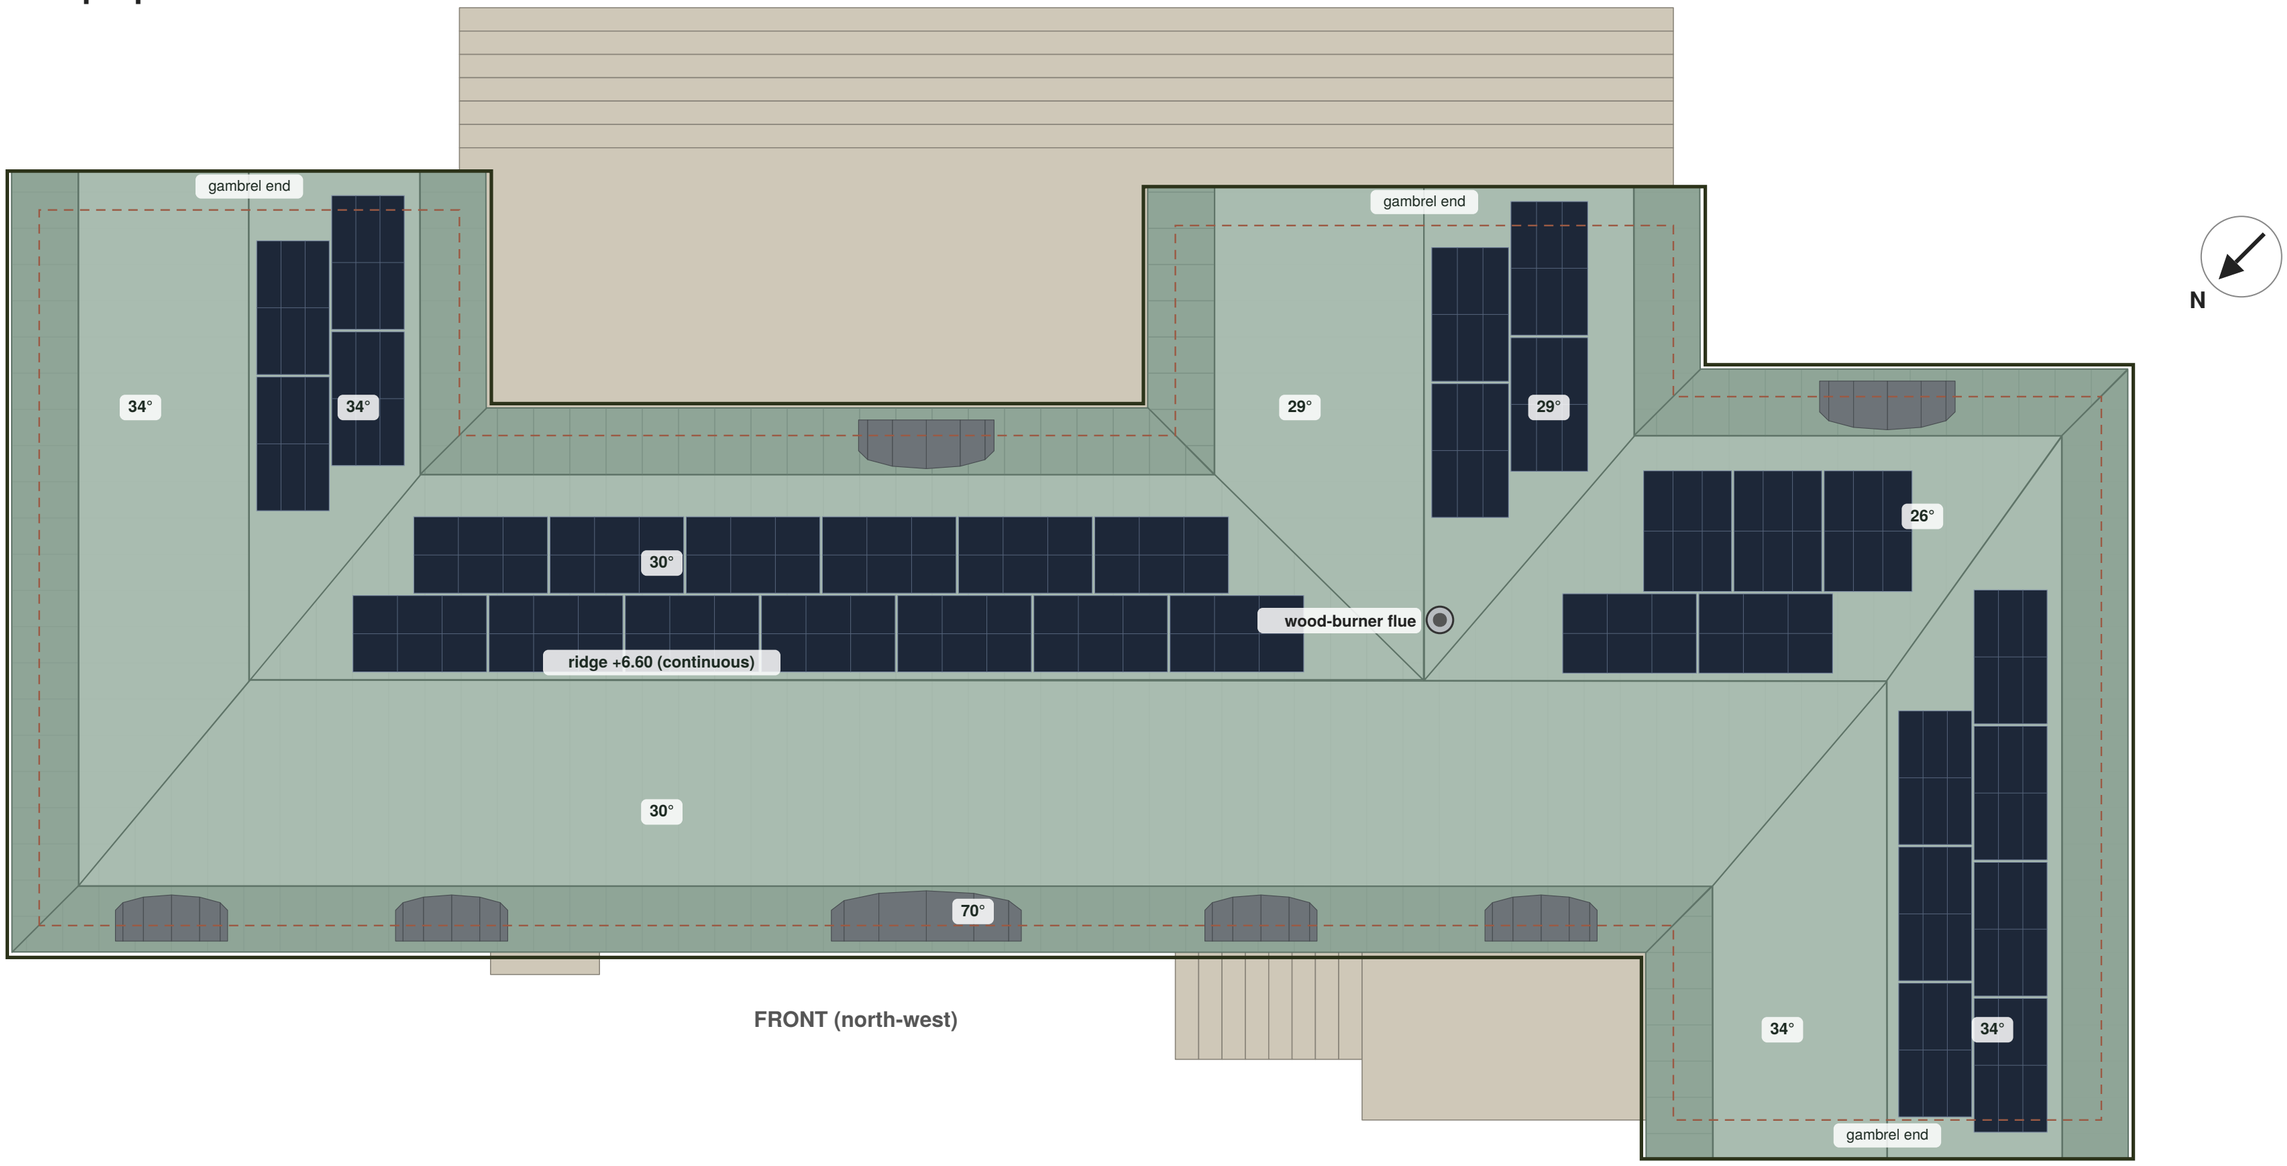

70° cladding over vertical frame (0.35 m overhang)

upper slopes (pitches set so every ridge = +6.60)

lead dormer hoods

solar PV — 33 standard 1.72×1.13 m panels ≈ 14.5 kWp (SE & SW slopes)

white boarded dormer faces

external walls below

thick line = gutter / verge — 0.35 m overhang to all walls, 0.5 m at gambrel ends · patina-green standing seam

0 5 m